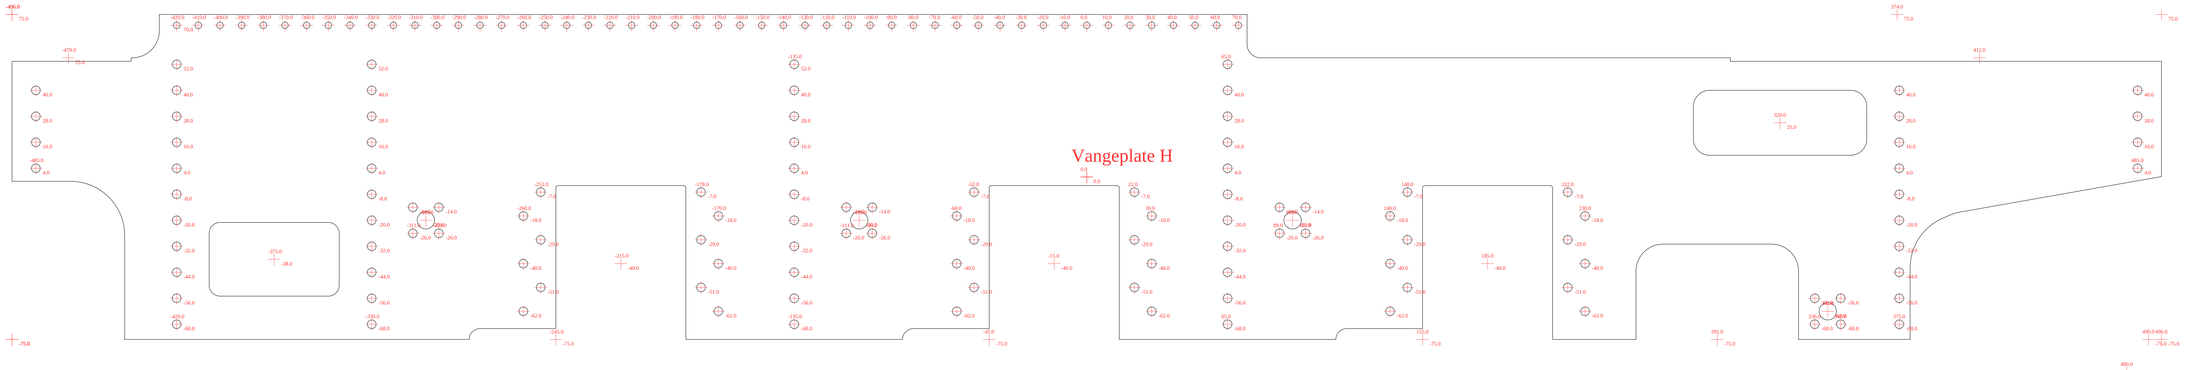

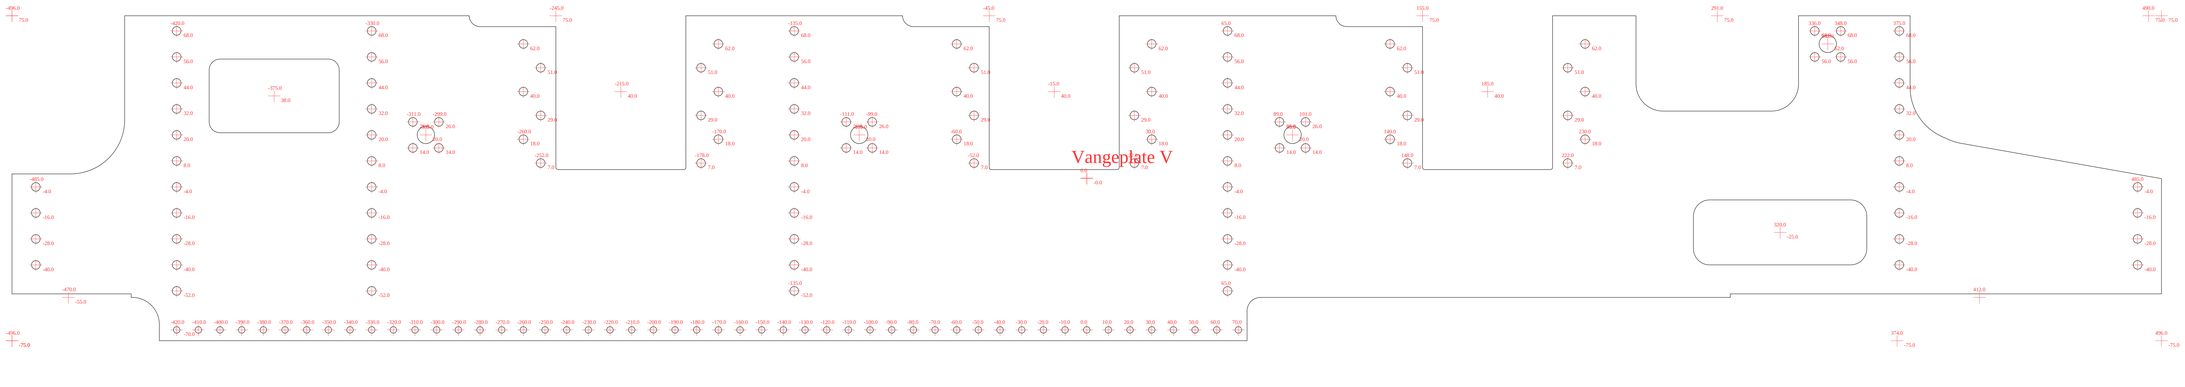

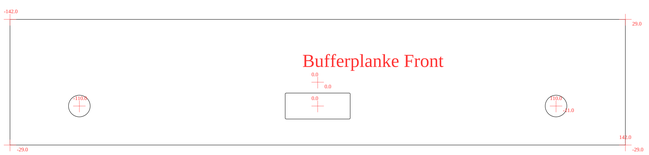

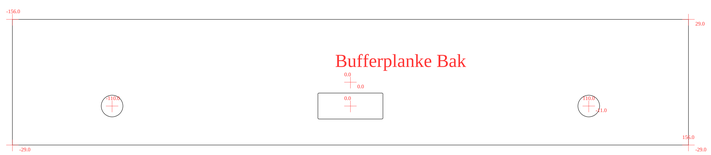

Modell Type 23
Sidevanger og bufferplanker
5mm staalplater
NMDF/2016-12-15/Aeo **Ark 1**

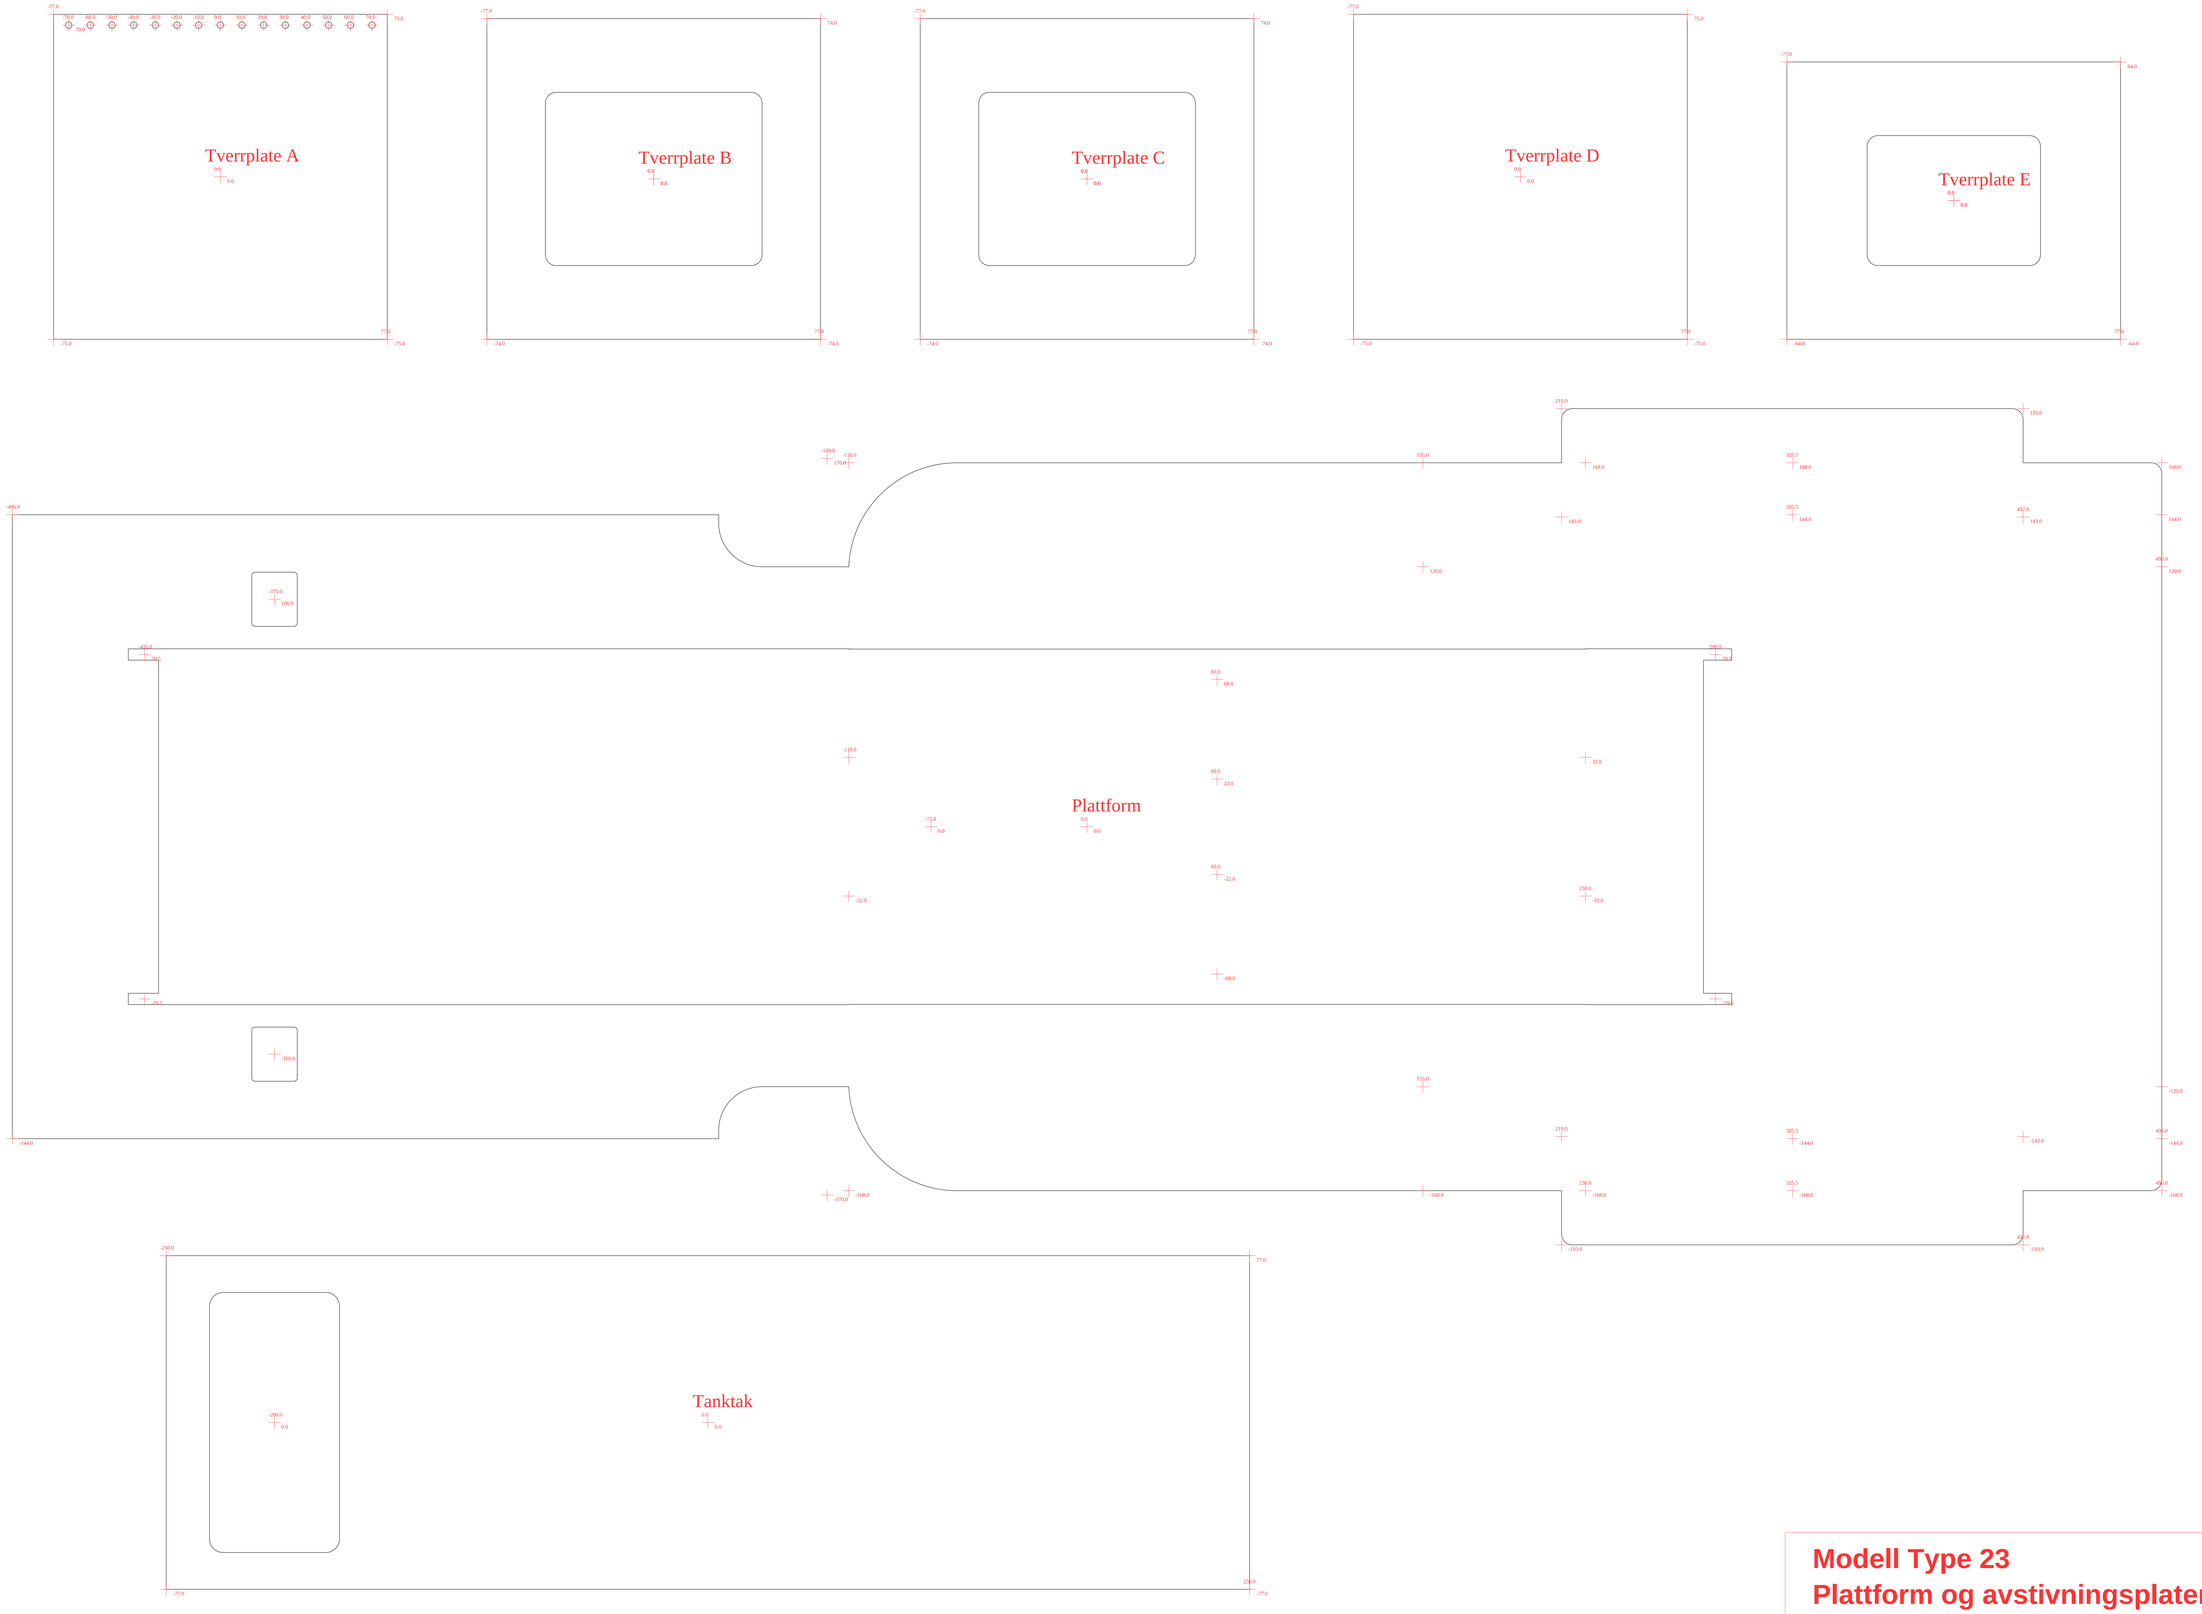

Modell Type 23
Plattform og avstivningsplater
2mm staalplater
NMDF/2016-12-15/Aeo **Ark 2**