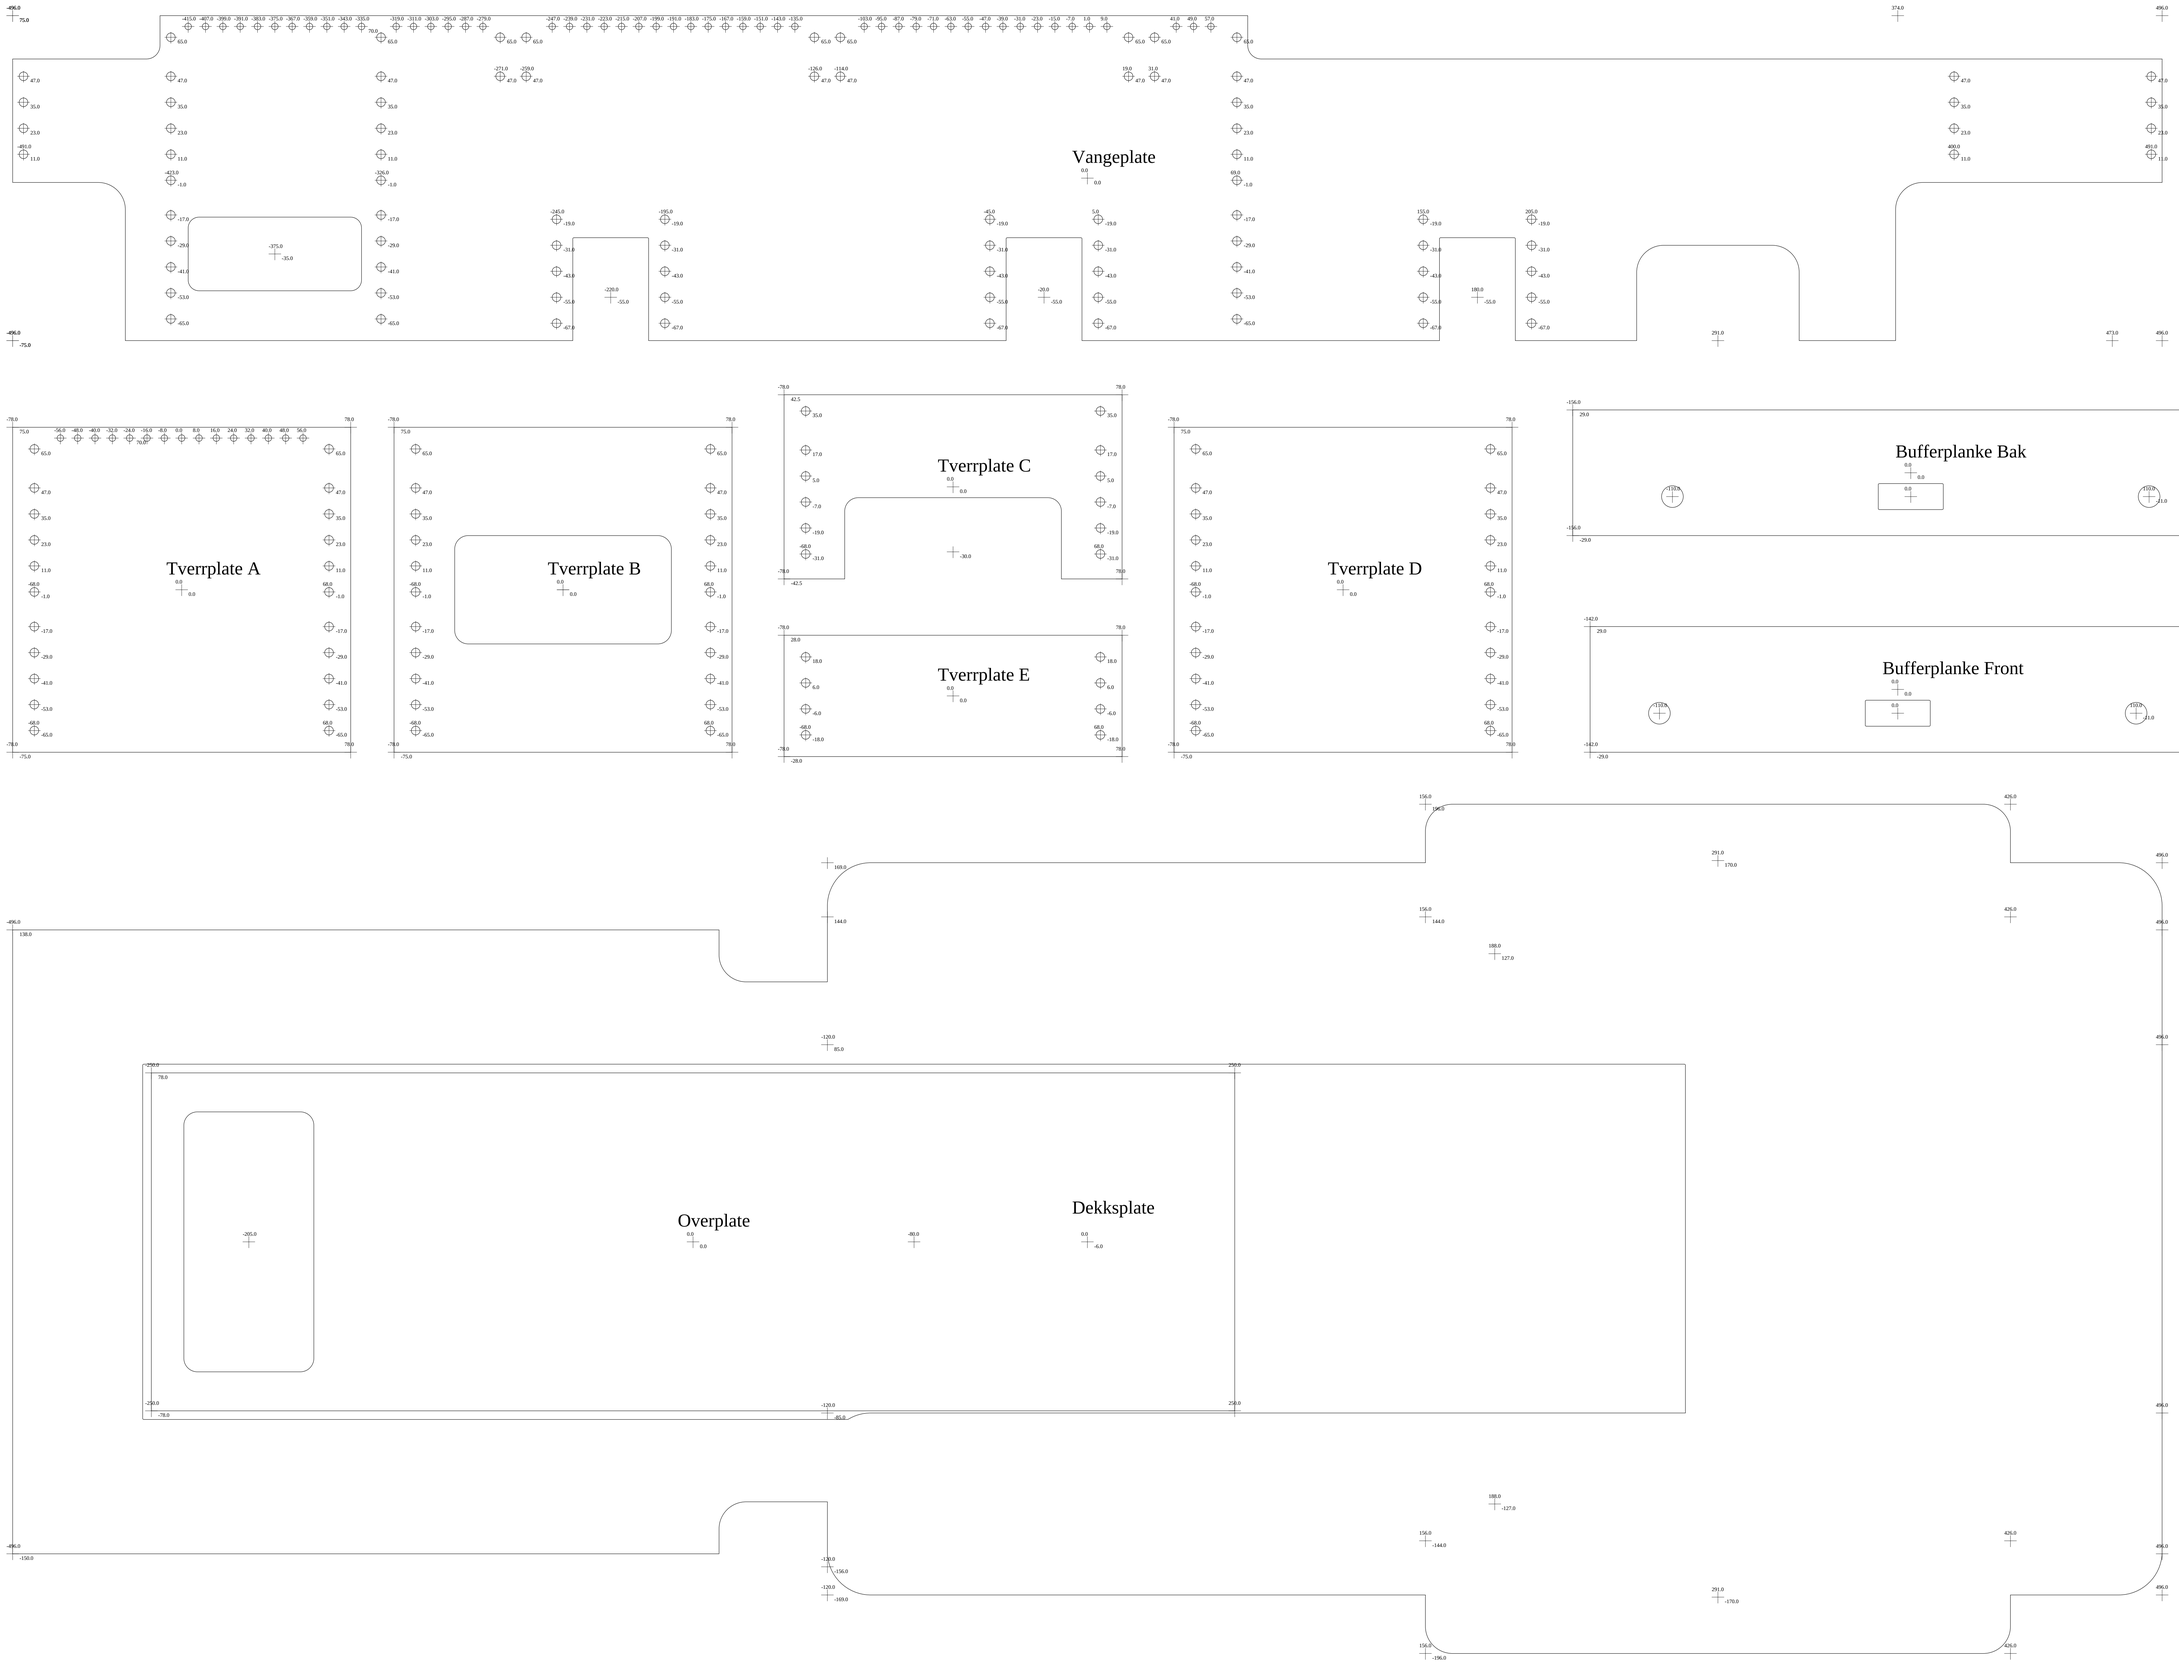
Vangeplate
Tverrplate A
Tverrplate B
Tverrplate C
Tverrplate D
Tverrplate E
Bufferplanke Bak
Bufferplanke Front
Overplate
Dekksplate